




REPUBLIKA E KOSOVËS / REPUBLIKA KOSOVA / REPUBLIC OF KOSOVO
QEVERIA E KOSOVËS / VLADA KOSOVA / GOVERNMENT OF KOSOVA

MINISTRIA E EKONOMISË DHE AMBIENTIT / MINISTARSTVO EKONOMIJE I ŽIVOTNE SREDINE / MINISTRY OF ECONOMY AND ENVIRONMENT

AGJENCIA KADASTRALE E KOSOVËS / KATASTARSKA AGENCIJA KOSOVA / KOSOVA CADASTRAL AGENCY

Raport i njësisë kadastrale

Zonë kadastrale: Lloshkobare
Lloji i njësisë kadastrale: Parcelë
Nr i njësisë kadastrale: P-72217056-00907-4

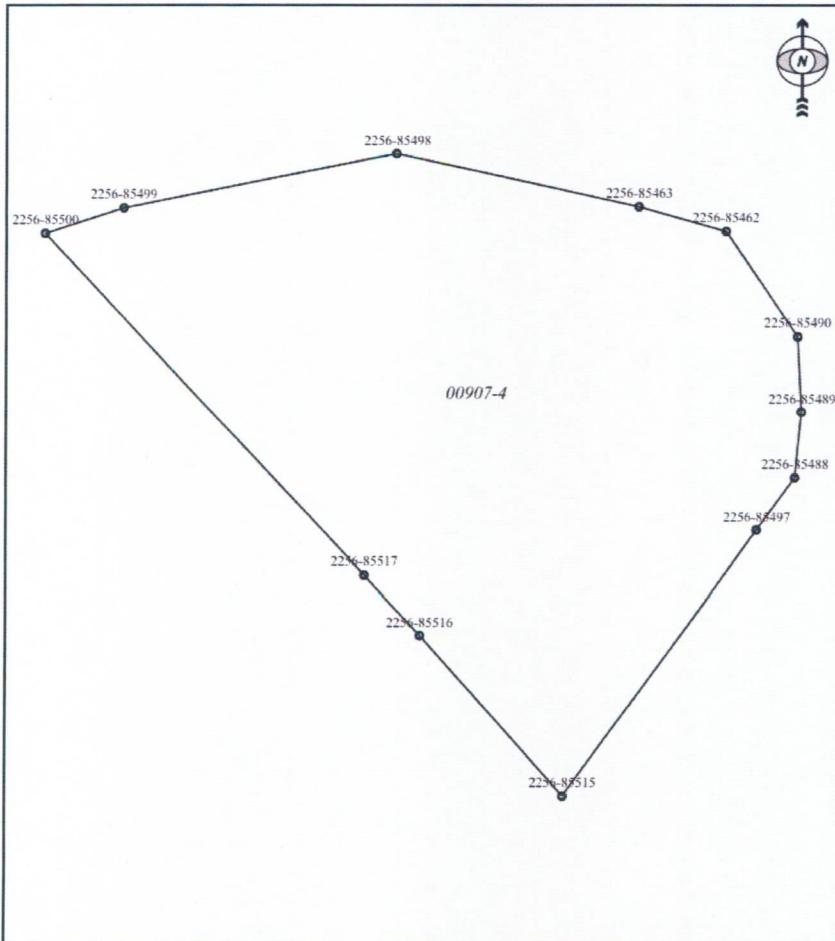

| Pika | Y | X |
|------------|-------------|-------------|
| 2256-85499 | 7511123.853 | 4693834.863 |
| 2256-85498 | 7511144.119 | 4693838.872 |
| 2256-85463 | 7511162.109 | 4693834.970 |
| 2256-85462 | 7511168.581 | 4693833.135 |
| 2256-85490 | 7511173.901 | 4693825.322 |
| 2256-85489 | 7511174.179 | 4693819.724 |
| 2256-85488 | 7511173.688 | 4693814.791 |
| 2256-85497 | 7511170.858 | 4693810.895 |
| 2256-85515 | 7511156.545 | 4693791.194 |
| 2256-85516 | 7511145.919 | 4693803.158 |
| 2256-85517 | 7511141.778 | 4693807.571 |
| 2256-85500 | 7511117.992 | 4693832.963 |

S. graf. 1458.2m²

Krijuar nga

Pozita:

Emri: Fadil

Mbiemri: Ibishi

Emri i shfrytëzuesit(kodi): Fadil.Ibishi

Data: 26.08.2020

Koha: 10:53:30

Nenshkrimi:





REPUBLIKA E KOSOVËS / REPUBLIKA KOSOVA / REPUBLIC OF KOSOVO

QEVERIA E KOSOVËS / VLADA KOSOVA / GOVERNMENT OF KOSOVA

MINISTRIA E EKONOMISË DHE AMBIENTIT / MINISTARSTVO EKONOMIJE I ŽIVOTNE SREDINE / MINISTRY OF ECONOMY AND ENVIRONMENT

AGJENCIA KADASTRALE E KOSOVËS / KATASTARSKA AGENCIJA KOSOVA / KOSOVA CADASTRAL AGENCY

Raport i njësisë kadastrale

Scale: 1:515

Proceset paraprake:

| Rasti | ID e Procesit | Lloji i procesit: | Data | Perdoruesi |
|-------|---------------|---|-------------|------------|
| | 194956 | Zëvendësimi i zonës kadastrale ekzistuese | 20.05.2019. | geocad1 |

Krijuar nga

Pozita:

Emri: Fadil

Mbiemri: Ibishi

Emri i shfrytëzuesit(kodi): Fadil.Ibishi

Data: 26.08.2020

Koha: 10:53:30

Nenshkrimi:






REPUBLIKA E KOSOVËS / REPUBLIKA KOSOVA / REPUBLIC OF KOSOVO
QEVERIA E KOSOVËS / VLADA KOSOVA / GOVERNMENT OF KOSOVA

MINISTRIA E EKONOMISË DHE AMBIENTIT / MINISTARSTVO EKONOMIJE I ŽIVOTNE SREDINE / MINISTRY OF ECONOMY AND ENVIRONMENT

AGJENCIA KADASTRALE E KOSOVËS / KATASTARSKA AGENCIJA KOSOVA / KOSOVA CADASTRAL AGENCY

Raport i njësisë kadastrale

Zonë kadastrale: Lloshkobare
Lloji i njësisë kadastrale: Parcelë
Nr i njësisë kadastrale: P-72217056-00908-1

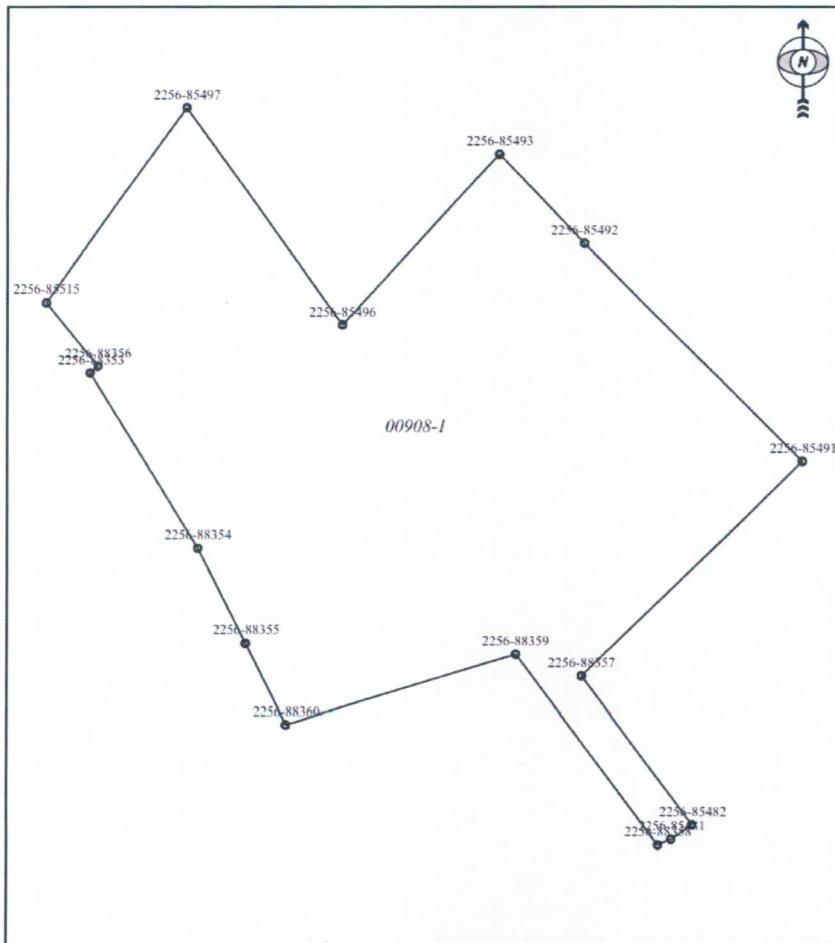

| Pika | Y | X |
|------------|-------------|-------------|
| 2256-88354 | 7511172.047 | 4693766.179 |
| 2256-88353 | 7511161.029 | 4693783.957 |
| 2256-88356 | 7511161.818 | 4693784.656 |
| 2256-85515 | 7511156.545 | 4693791.194 |
| 2256-85497 | 7511170.858 | 4693810.895 |
| 2256-85496 | 7511186.754 | 4693788.926 |
| 2256-85493 | 7511202.687 | 4693806.158 |
| 2256-85492 | 7511211.309 | 4693797.147 |
| 2256-85491 | 7511233.408 | 4693774.915 |
| 2256-88357 | 7511211.056 | 4693753.051 |
| 2256-85482 | 7511222.257 | 4693738.038 |
| 2256-85481 | 7511220.140 | 4693736.581 |
| 2256-88358 | 7511218.788 | 4693735.998 |
| 2256-88359 | 7511204.389 | 4693755.272 |
| 2256-88360 | 7511181.030 | 4693748.158 |
| 2256-88355 | 7511176.924 | 4693756.395 |

S. graf. 2715.3m²

Krijuar nga

Pozita:

Emri: Fadil

Mbiemri: Ibishi

Emri i shfrytëzuesit(kodi): Fadil.Ibishi

Data 26.08.2020

Koha: 10:55:57

Nenshkrimi:





REPUBLIKA E KOSOVËS / REPUBLIKA KOSOVA / REPUBLIC OF KOSOVO

QEVERIA E KOSOVËS / VLADA KOSOVA / GOVERNMENT OF KOSOVA

MINISTRIA E EKONOMISË DHE AMBIENTIT / MINISTARSTVO EKONOMIJE I ŽIVOTNE SREDINE / MINISTRY OF ECONOMY AND ENVIRONMENT

AGJENCIA KADASTRALE E KOSOVËS / KATASTARSKA AGENCIJA KOSOVA / KOSOVA CADASTRAL AGENCY

Raport i njësisë kadastrale

Scale: 1:705

Proceset paraprake:

| Rasti | ID e Procesit | Lloji i procesit: | Data | Perdoruesi |
|-------|---------------|---|-------------|------------|
| | 194956 | Zëvendësimi i zonës kadastrale ekzistuese | 20.05.2019. | geocad1 |

Krijuar nga

Pozita:

Emri: Fadil

Mbiemri: Ibishi

Emri i shfrytëzuesit(kodi): Fadil.Ibishi

Data 26.08.2020

Koha: 10:55:57

Nenshkrimi:





Numri i Protokollit

194/2020

Republika e Kosovës
Republika Kosova-Republic of Kosova
Qeveria -Vlada-Government

Ministria e Mjedisit dhe Planifikimit Hapësinor /Ministarstvo Sredine i Prostornog Planiranja/ Ministry of Environment and Spatial Planning
AGJENCIA KADASTRALE E KOSOVËS/ KATASTARSKA AGENCIA KOSOVA/ KOSOVA CADASTRAL AGENCY

Formulari nr. 5

KËRKESË PËR SHERBIMET KADASTRALE NGA GJEODETI APO KOMPANIJA GJEODETE E LICENCUAR

| | |
|--|-----------------------|
| Gjeodeti / Kompania gjeodete e licencuar: Liridon Sejdiu | Numri i licencës: 140 |
|--|-----------------------|

| | |
|-----------------|------------------------------|
| Komuna: Ferizaj | Zona Kadsatrale: Lloshkobare |
|-----------------|------------------------------|

| |
|---|
| Numri i njësisë kadastrale: 00908-1,00907-4 |
|---|

1. Të dhënat për parashtruesin e kërkesës

| | | |
|--------------------------------|-----------------------------------|--------------------------|
| Emri / Emri i Kompanisë: BUJAR | Mbiemri: MISINI | Emri i prindit: BAJRUSH |
| Numri personal: 1170142531 | Adresa: Ferizaj Rr. "Haxhi Sejda" | Nr. Tel: +383 44 413 440 |

2. Parashtruesi i kërkesës: Pronar - Shfrytëzues - Përfaqësues i Autorizuar

3. Lista e dokumenteve të nevojshme:

| Pronari/Shfrytëzuesi | Përfaqësues i Autorizuar |
|--|---|
| 1 <input checked="" type="checkbox"/> Letërnjoftimin / Certifikatë biznesi (kopje) | 1 <input type="checkbox"/> Letërnjoftimin / Certifikatë biznesi (kopje) |
| 2 <input checked="" type="checkbox"/> Vërtetimi i tatimit në pronë | 2 <input type="checkbox"/> Vërtetimi i tatimit në pronë |
| 3 <input type="checkbox"/> Çertifikata e pronës | 3 <input type="checkbox"/> Çertifikata e pronës |
| 4 <input type="checkbox"/> Kopja e planit | 4 <input type="checkbox"/> Kopja e planit |

4. Kërkesa për:

| | |
|--|--|
| 1 <input type="checkbox"/> Ndërrim të kulturës së parcelës | 6 <input type="checkbox"/> Matjen dhe regjistrimin e ndërtesës |
| 2 <input checked="" type="checkbox"/> Ndarjen e parcelës | 7 <input type="checkbox"/> Matjen dhe regjistrimin e pjesës së ndërtesës |
| 3 <input checked="" type="checkbox"/> Bashkimin e parcelës | 8 <input type="checkbox"/> Punë të veçanta gjeodezike |
| 4 <input type="checkbox"/> Përcaktimin e kufijve të parcelës | 9 <input type="checkbox"/> Matja e ndërtesës për legalizim |
| 5 <input checked="" type="checkbox"/> Ri-rregullimin e kufirit të parcelës | 10 <input type="checkbox"/> Riregjistrim i pjesës grafike |

Nënshkrimi: _____



Data: 28.08.2020

Gjeodeti i licecnuar: SH.P.K. "GEO CODING" Numri i licencës: 140

Adresa: Rruga "Shkëlzen Haradinaj" - Ferizaj



Data: 25.08.2020 14:22:56

| | | |
|--|----------------------|--|
| DEBI: | | 20.00 |
| KREDI: | | 21.00 |
| PROVIZIONI: | | 1.00 |
| LLOGARIA: | KOMUNA FERIZAJ | |
| NUMRI I LLOGARISE: | 1000650030000035 | |
| REFERENCA: | FEG9D2520001955N | |
| PAGOI: | LIRIDON SEJDIU | |
| NR.SERIK: | 2520001955 | |
| PERSHKRIMI: | 10-942/05-0068395/20 | |
| PER IFJB CAPITAL SH.P.K. | | KERKSE PER BLERJEN E PRODUKTEVE KADASTRALE |
| <p style="text-align: center;">Arkatarj: 25-08-2020 </p> | | Shendrit Shabani B.I sh.shabani |
| | | Pagoi: |



REPUBLIKA E KOSOVËS - REPUBLIKA KOSOVA - REPUBLIC OF KOSOVA

KOMUNA FERIZAJ - OPŠTINA UROŠEVAC - MUNICIPALITY OF FERIZAJ

DREJTORIA E PRONËS, KADASTRIT DHE GJEODEZISË



FATURE-RACUN-INVOICE

Nr. Serik/ Ser Br./ Ser No
2520001955

NF/FN/NB600629804

Emri/Mbiemri
Ilme/Prezime
Name/Surname

Liridon Sejdiu

Pershkrimi
Opis
Description10-942/05-0068395/20 - Kerkes per blerjen e produktave
kadastrale me nr. 00908-1,00907-4 Zk LloshkobShuma
Iznos
Amount

20.00


Data
Datum
Date

25/08/2020

Llogaria Bankare
Broj Ziroracuna
Bank Account

1000650030000035



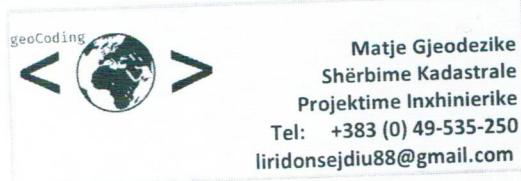

N.SH. "Geo Coding"

Faturë

Nr: 27/2020

| | |
|---------------|-----------------------------|
| Shitësi: | N.SH. "Geo Coding" |
| Pronari: | LIRIDON SEJDIU |
| NRB: | 811384528 |
| Numri Fiskal: | 811384528 |
| Adresa: | Rr. "12 Qershori" - Ferizaj |
| | BPB - 13-04-0010027832.69 |
| LL/Bankare | 130400100278326000.00% |

| | |
|-------------|---------------------|
| Blerësi: | Bajrush (Ukë) Msini |
| Nr. ID. | 1013067666 |
| NRB: | |
| Nr. Fiskal: | |
| Adresa: | |
| LL/Bankare | |

| Nr. | Përshkrimi | Njësi matëse | Sasia | Çmimi | Vlera totale |
|---------|--|--------------|-------|---------|--------------|
| 1 | Bashkim i parcelave me nr. 00907-4,00908-1 në Z.K. Lloshkobare | cop | 2 | 10.00 | 20.00 |
| | | | | | - |
| | | | | | - |
| | | | | | - |
| | | | | | - |
| | | | | | - |
| Totali: | | | | € 20.00 | |

Data: 29.08.2020

Pagesa: Cash

Komenti: 1. BPB 13-04-0010027832.69
2. Banka Ekonomike 1304001002783269

Pranoi:



Dorëzoj:



Republika e Kosovës

Republika Kosova - Republic of Kosovo

Qeveria e Kosovës - Vlada Kosova - Government of Kosovo

Ministria e Infrastrukturës dhe Ambientit/ Ministrastvo Infrastrukture i Sredine/ Ministry of Infrastructure and Environment

AGJENCIA KADASTRALE E KOSOVËS/ KOSOVSKA KATASTARSKA AGENCIJA/ KOSOVA CADASTRAL AGENCY

MBËSHTJELLËS I LËNDËS

Gjeodeti / Kompania gjeodete e licencuar: **LIRIDON SEJDIU**

Numri i licencës: **140**

Numri i Protokollit: **194/2020**

LËNDA:

1. Ndërrim të kulturës së parcelës
2. Ndarjen e parcelës
3. Bashkimin e parcelës
4. Përcaktimin e kufijve të parcelës
5. Ri-rregullimin e kufirit të parcelës
6. Matjen dhe regjistrimin e ndërtesës
7. Matjen dhe regjistrimin e pjesës së ndërtesës
8. Regjistrimi i servitutit
9. Punë të veçanta gjeodezike
10. Matja e ndërtesës për legalizim

“GJEODET I LICENCUAR”

+383 49 535 250

e-mail: liridonsejdiu88@gmail.com

Data: **29/08/2020**

Vendi: **FERIZAJ**

.....

(Nënshkrimi dhe vula)

Përbajtja:

1. Kërkesa e palës
 2. Dëshmia e burimit të të dhënave zyrtare
 3. Dëshmia e pagesës për të dhënat e pranuara
 4. Fatura apo kuponi fiskal e lëshuar shërbimet kadastrale sipas UA 11/2019 dhe 12/2019
 5. Procesverbali nga terreni
 6. Manuali i njësive kadastrale
 7. Regjistri i ndërrimeve
 8. Lista e koordinatave të matura
 9. Formulari i korrigjimit të sipërfaqes
 10. Leternjoftimi i pronarit
 11. Certifikatën e pronësisë
 12. Raporti teknik
 13. Leternjoftimi kopje i fqinjëve
 14. Dokumentacioni i gjeodetit të licencuar

Dokumente tjerar:



REPUBLIKA E KOSOVËS
РЕПУБЛИКА КОСОВО
REPUBLIC OF KOSOVO

LETENJOFTIM / ЛИЧНА КАРТА / IDENTITY CARD

Mbiemri/Презиме/Name

MISINI

Emri/Име/First name

BAJRUSH

Gjinie/Пол/Sex

M

Data e lindjes/Датум рођења/Date of birth

08.03.1934

Vendi i lindjes/Место рођења/Place of birth

LLOSHKOBARE

Dati e skadimit/Датум истека/Date of expiry

Përhershëm/Trajna/Permanent



DATA E LEŠIMIT/ДАТУМ ИЗДАВАЊА/Date of issue

02.03.2010

LESHUAR NGA/СЛУЖБА КОЈА ИЗДАЈЕ/Issuing authority

MPB / MUP / MIA

NUMRI PERSONAL/ЛИЧНИ БРОЈ/Personal number

1013067666

QKRC/OIHP/MCRC

2501S

Nr Inj/Бр. ик/Id.no

ID03104012



REPUBLIKA E KOSOVËS
LËTËRNUOTITIM

РЕПУБЛИКА КОСОВО
ЛІЧНА КАРТА

REPUBLIC OF KOSOVO
IDENTITY CARD



Emri / Презиме / Surname

MISINI

Emri / Име / Given name

BUJAR

Datelindja / Датум рођења / Date of birth

19.10.1974

Nacionalitet / Држављанство / Nationality

KOSOVAR

Vredninja / Место гођења / Place of birth

FERIZAJ

Nenshkrimi / Потпис / Signature

Gjina / Пол / Sex

M

Data e skadimit / Датум истека / Date of expiry

07.12.2026

887735

Data e lëshimit / Датум издавања / Date of issue
08.12.2016
Leshuar nga / Издат од / Issued by
MPB / MUP / MIA
Nr. Personal / Лични број / Personal No
1170142531
Nr. Lni / Број ЛН / ID Card No
ID0659764
Vendlindje / Пребивалиште / Residence
FERIZAJ

IDRKSID06597642<<<<<<<<<<
7410194M2612074RKS1170142531<1
MISINI<<BUJAR<<<<<<<<<<<<



Republika e Kosovës / Republika Kosova / Republic of
Komuna e FERIZAJ / Opština UROŠEVAC / Municipality



Bazuar në nenin 18 të ligjit 03/L-204 për tatimin në pronë, si dhe udhëzimit administrativ nr. 7/2011 të lëshuar nga MF, i cili ka të bëjë me urdhëresat e ndalimit të shërbimeve komunale për detyrim të pagesës së tatimit në

Na osnovu člana 18, zakona 03/L-204 za poreza na imovinu i administrativne uredbe MF br. 7/2011, u vezi zabrane opštinske usluga za prinudu uplate poreza na imovinu, izdaje se ova:

Based on the article 18 of LAW 03/L-204 on property tax and administrative instruction MF no. 7/2011 on termination of services for enforcement of the municipal property tax, the municipal Property Tax Office

Nr / Br / No

22510188

25/08/2020

VËRTETIM
POTVRDA
CERTIFICATE

Me të cilin vërtetohet se tatimpaguesi

Kojim se potvrđuje da je poreznik
that certifies that taxpayer

BAJRUSH MISINI

FERIZAJ

Komuna / Opština / Municipality

FERIZAJ BRAHIM ADEMI PN.

adresa / address

I ka kryer pjesërisht / plotësisht obligimet e tatimit në pronë

Delirnično/ izveršio uplatu poreskih obaveza

has partially / fulfilled obligations on property tax

BAJRUSH UKE MISINI

Vërtetimi lëshohet në bazë të kërkesës së / Potvrda se izdaje na zahtev / Certificate is issued by

Për nevoja personale

dhe shërbën për / i služi za / and is used for

Shënimë shtesë / Druge podatke / Additional info



Nenshkrimi / Potpis / Signature



Republika e Kosovës
Republika Kosova-Republic of Kosovo
Qeveria e Kosovës- Vlada Kosova- Government of Kosovo
Ministria e Infrastrukturës dhe Ambientit/ Ministrastvo Infrastrukture i Sredine/ Ministry of
Infrastructure and Environment

AGJENCIA KADASTRALE E KOSOVËS/KOSOVSKA KATASTARSKA AGENCIJA/ KOSOVO CADASTRAL AGENCY

PROCESVERBALI NGA TERRENI

| | |
|--|-------------------------------------|
| Gjeodeti / Kompania gjeodete e licencuar: Liridon Sejdiu | Numri i licencës: 140 |
| Komuna: Ferizaj | Zona Kadastrale: #LL0SHKOBREG |
| Numri i njësisë kadastrale: 908-1,907-4 | |
| Matja/piketimi është realizuar me: | |
| GPS/GNSS | <input checked="" type="checkbox"/> |
| Stacion Total | <input type="checkbox"/> |

1. Përshkimi i procesit:

*DHE QËKJA
 TË PARC. TË /ARTËCFKURA/ DHE QËKJA
 TË NDARJES. PËESA VERiore E PARC. NDAHET S/PAS GJENDJES
 FAKTIKE/RRUGA), KURSE PËESA TUGORE S/PAS S/P. TË
 KUSHTËZUAR DHE S/P. TË BARBTARTA, LINDJA E NDARJUE
 NË NORMALE TË FUNDIT TË PAR C.*

2. Vërejtje:

3. Nënshkrimi i palëve

Pronarët janë pajtuar me pikat definitive kufitare të vendosura në terren nga të cilat derivohet sipërfaqja definitive që do të regjistrohet në Sistemin e Informacioneve Kadastrale për Tokën në Kosovë.

Të poshtëshënuarve u lexohet procesverbalı dhe nëse pajtohen me atë nënshkruajnë më poshtë, në të kundërtën jepin arsyet e mospajtimit.

| Emri (emri i prindit) mbiemri | Numri personal | Numri i njësisë kadastrale | Nënshkrimi |
|-------------------------------|----------------|----------------------------|--------------------|
| DEFUNI MISINI | 1012210564 | 908-1,907-4 | <i>[Signature]</i> |
| BASIRUSH MISINI | 1013267666 | | <i>[Signature]</i> |
| BUSAR MISINI | 1170191531 | | <i>[Signature]</i> |

Nënshkrimi dhe vula e gjodetit: *[Signature]* Data: 18.01.2020



Republika e Kosovës
Republika Kosova-Republic of Kosova
Qeveria - Vlada-Government
Ministria e Mjedisit dhe Planifikimit Hapësinor /Ministarstvo Sredine i Prostornog Planiranja/Ministry of Environment and Spatial Planning
AGJENCIJA KADASTRALE E KOSOVËS/ KATASTARSKA AGECIJA KOSOVA/ KOSOVA CADASTRAL AGENCY

Zyra kadastrale komunale / Opštinska katastarska kancelarija: Ferizaj


Nr. i njësisë kadastrale / Br. katastarske jedinice : 907-4, 908-1

Zona kadastrale / Katastarska zona: Lloshkobare

Numri i lëndës / Broj predmeta: _____

Lloji i njësisë kadastrale / Vrsta katastarske jedinice : Parcel

Shkalla e zvoglimit / Razmera plana : 1:1000

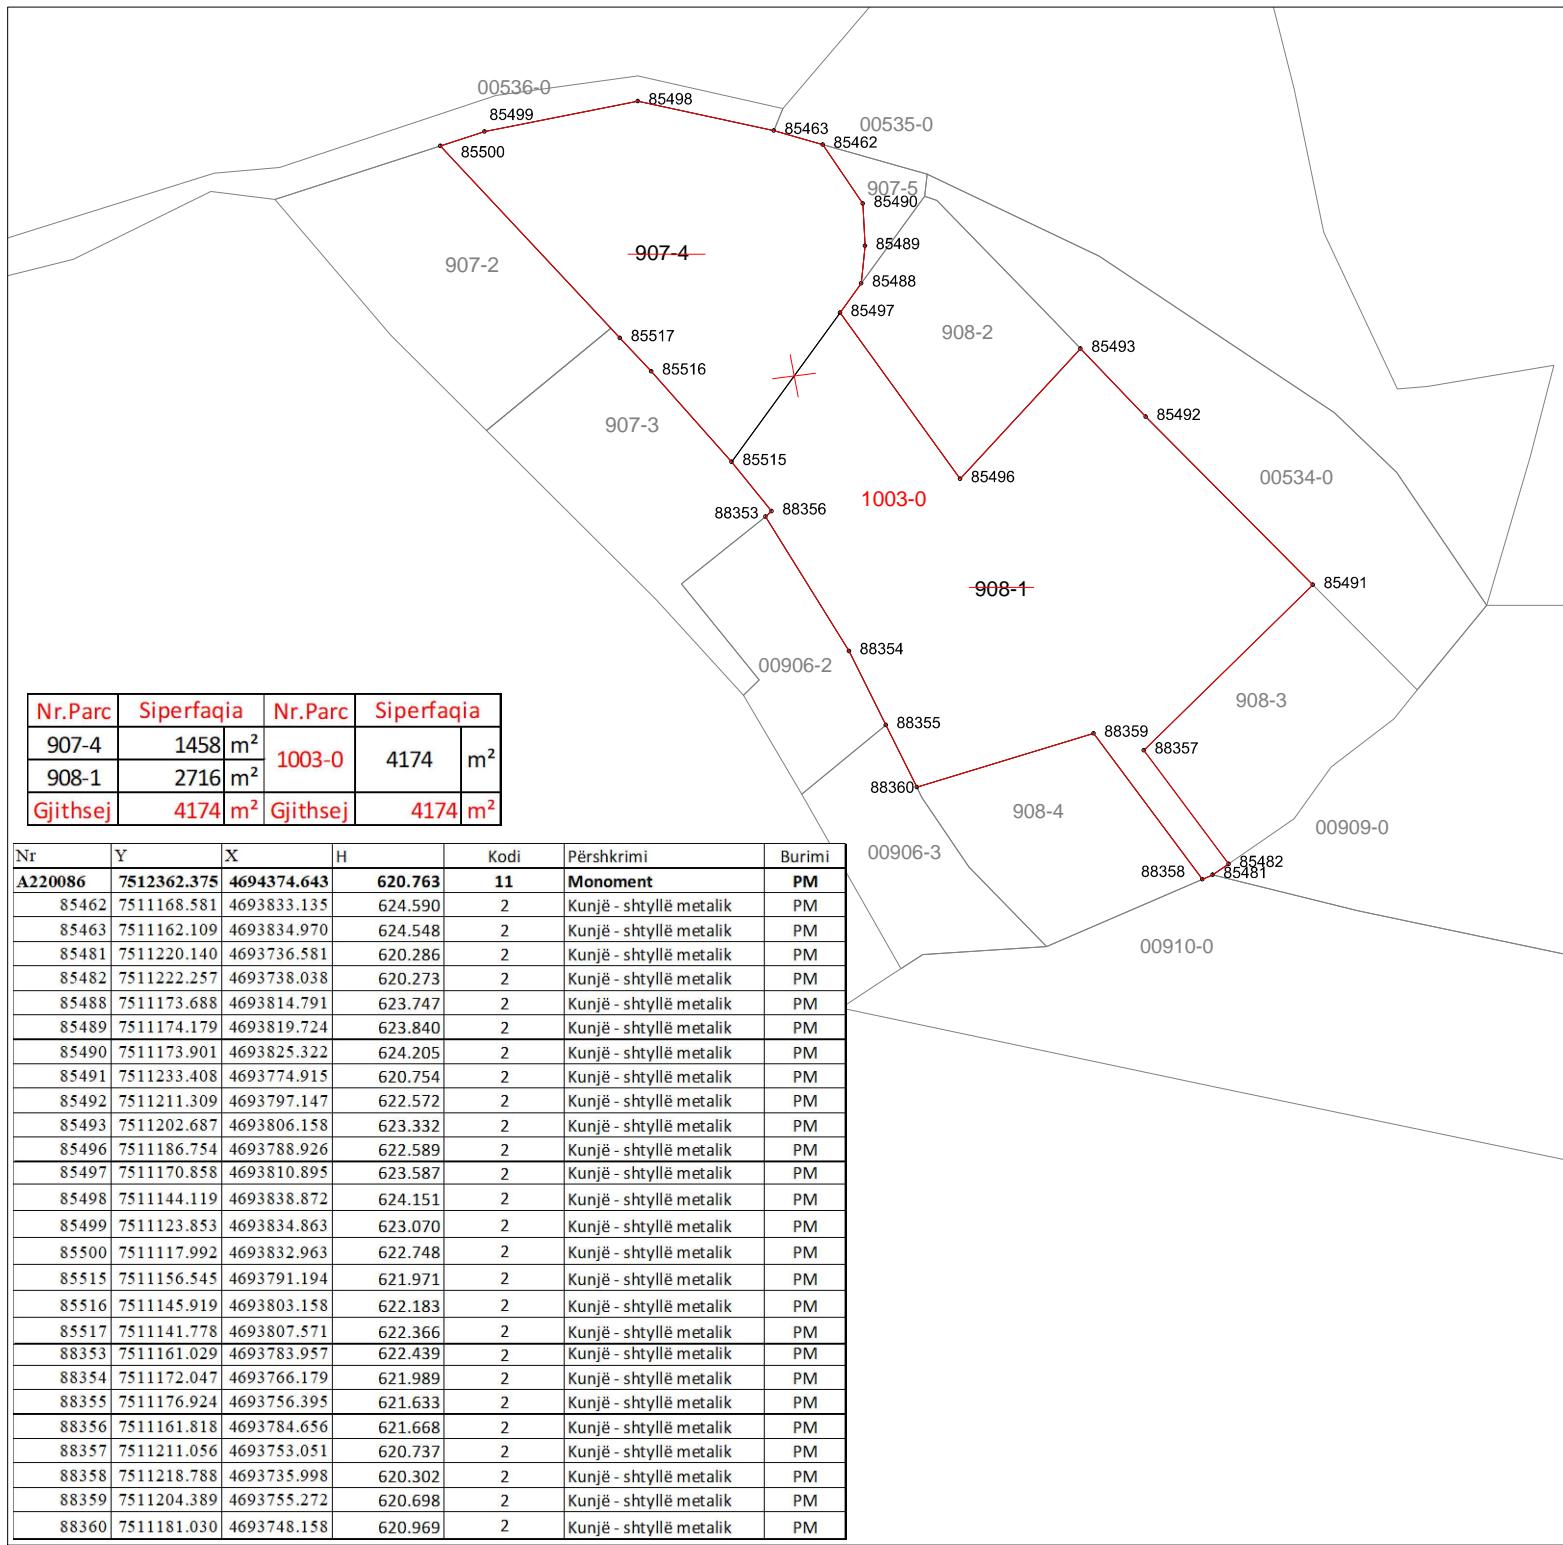

Rilevoi / Snimio: LIRIDON SEJDIU

(emri dhe mbiemi i gjedjetit/kompanisë/ ime i prezime geodeta/ kompanije)

Nr. i licencës / Br. licence: 140

V.V.

Nënshkrimi / Potpis: _____

Data e rilevimit / Datum snimanja: 28.08.2020

Aprovoi / Usvojio: _____

(emri dhe mbiemi i pësonit zyrtar/ ime i prezime sluzbenog lica)

Nënshkrimi / Potpis: _____

Data e aprovimit / Datum usvajanja: _____



| Open Documents | |
|-------------------|--|
| 908-1-Lloshkobare | |

| Point Id | Point Class | Date/Time | Easting | Northing | Ellip. Hgt. | Code | Posn. + Hgt. Qty |
|-----------------|-------------|---------------------|--------------|--------------|-------------|------|------------------|
| ✓ 100 | Measured | 08/28/2020 15:57:32 | 7511171.8967 | 4693771.2558 | 621.3436 | GURI | 0.0140 |
| ✓ 102 | Measured | 08/28/2020 16:25:19 | 7511161.2269 | 4693832.3151 | 624.5315 | | 0.0281 |
| ✓ 103 | Measured | 08/28/2020 16:25:35 | 7511166.0254 | 4693828.7019 | 624.3439 | | 0.0204 |
| ✓ 104 | Measured | 08/28/2020 16:27:45 | 7511168.0846 | 4693826.2940 | 624.2672 | | 0.0228 |
| ✓ 105 | Measured | 08/28/2020 16:27:53 | 7511169.2512 | 4693824.2651 | 624.2475 | | 0.0205 |
| ✓ 106 | Measured | 08/28/2020 16:28:02 | 7511169.8705 | 4693821.9633 | 624.1391 | | 0.0182 |
| ✓ 108 | Measured | 08/28/2020 16:29:55 | 7511170.0772 | 4693820.2812 | 624.0357 | | 0.0224 |
| ✓ 109 | Measured | 08/28/2020 16:30:12 | 7511169.9735 | 4693816.9881 | 623.8514 | | 0.0205 |
| ✓ 113 | Measured | 08/28/2020 16:35:59 | 7511169.5890 | 4693810.5449 | 623.5087 | | 0.0186 |
| ✓ 114 | Measured | 08/28/2020 16:36:12 | 7511169.6092 | 4693808.3095 | 623.3709 | | 0.0269 |
| ✓ 115 | Measured | 08/28/2020 16:36:21 | 7511170.8049 | 4693804.9265 | 623.2276 | | 0.0199 |
| ✓ A1 | Measured | 08/28/2020 16:37:44 | 7511172.7502 | 4693808.3622 | 623.5148 | | 0.0231 |
| ✓ A2 | Measured | 08/28/2020 17:49:52 | 7511154.4766 | 4693793.5636 | 621.9991 | | 0.0152 |
| ✓ A3 | Measured | 08/28/2020 16:39:46 | 7511169.5975 | 4693805.8032 | 623.3161 | | 0.0196 |
| ✓ A4 | Measured | 08/28/2020 17:17:59 | 7511183.4392 | 4693786.6929 | 622.4624 | | 0.0384 |
| ✓ A5 | Measured | 08/28/2020 17:29:51 | 7511187.6921 | 4693780.2936 | 622.0582 | | 0.0400 |
| ✓ A6 | Measured | 08/28/2020 17:31:58 | 7511170.0808 | 4693769.3731 | 621.0177 | | 0.0167 |
| ✓ A7 | Measured | 08/28/2020 17:28:34 | 7511199.5931 | 4693769.8982 | 621.4339 | | 0.0223 |
| ✓ A8 | Measured | 08/28/2020 17:23:14 | 7511219.3042 | 4693789.0844 | 621.7804 | | 0.0248 |
| ✓ A85462 | Measured | 08/28/2020 16:26:52 | 7511168.6000 | 4693833.1421 | 624.5902 | | 0.0152 |
| ✓ A85463 | Measured | 08/28/2020 16:01:19 | 7511162.1376 | 4693834.9688 | 624.5481 | | 0.0207 |
| ✓ A85488 | Measured | 08/28/2020 16:32:00 | 7511173.6866 | 4693814.8416 | 623.7466 | | 0.0485 |
| ✓ A85489 | Measured | 08/28/2020 16:30:44 | 7511174.1914 | 4693819.7090 | 623.8395 | | 0.0182 |
| ✓ A85490 | Measured | 08/28/2020 16:29:35 | 7511173.9105 | 4693825.3670 | 624.2046 | | 0.0170 |
| ✓ A85497 | Measured | 08/28/2020 16:34:32 | 7511170.8777 | 4693810.9133 | 623.5937 | | 0.0287 |
| ✓ A85498 | Measured | 08/28/2020 16:02:56 | 7511144.1371 | 4693838.8702 | 624.1504 | | 0.0140 |
| ✓ A85499 | Measured | 08/28/2020 16:04:22 | 7511123.8333 | 4693834.8355 | 623.1091 | | 0.0295 |
| ✓ A85500 | Averaged | 08/28/2020 18:06:44 | 7511117.9878 | 4693832.9539 | 622.7480 | | 0.0173 |
| ✓ A85515 | Measured | 08/28/2020 17:48:52 | 7511156.5301 | 4693791.2523 | 621.9707 | | 0.0173 |
| ✓ A85516 | Measured | 08/28/2020 17:56:53 | 7511145.9046 | 4693803.1321 | 622.1833 | | 0.0149 |
| ✓ A85517 | Measured | 08/28/2020 17:57:36 | 7511141.7904 | 4693807.5469 | 622.3656 | | 0.0216 |
| ✓ A220086 | Measured | 08/28/2020 18:32:45 | 7512362.3748 | 4694374.6433 | 620.7631 | | 0.0451 |
| ✓ A736272 | Measured | 08/28/2020 17:45:39 | 7511172.0301 | 4693766.1273 | 622.0075 | | 0.0173 |
| ✓ A736273 | Measured | 08/28/2020 17:53:38 | 7511161.0437 | 4693783.9266 | 622.4387 | | 0.0151 |
| ✓ A736274 | Measured | 08/28/2020 17:52:52 | 7511161.8621 | 4693784.6247 | 621.6683 | | 0.0180 |
| ✓ A736275 | Measured | 08/28/2020 17:16:59 | 7511186.7516 | 4693788.9625 | 622.5930 | | 0.0298 |
| ✓ A736276 | Measured | 08/28/2020 17:20:40 | 7511202.6988 | 4693806.1289 | 623.3325 | | 0.0475 |
| ✓ A736277 | Measured | 08/28/2020 17:21:58 | 7511211.2675 | 4693797.1612 | 622.5724 | | 0.0263 |
| ✓ A736278 | Measured | 08/28/2020 17:24:59 | 7511233.4099 | 4693774.9483 | 620.7545 | | 0.0402 |
| ✓ A736279 | Measured | 08/28/2020 17:26:28 | 7511211.0289 | 4693753.0724 | 620.7371 | | 0.0331 |
| ✓ A736280 | Measured | 08/28/2020 17:35:44 | 7511222.3220 | 4693738.0208 | 620.2728 | | 0.0130 |
| ✓ A736286 | Measured | 08/28/2020 17:36:38 | 7511220.1578 | 4693736.5473 | 620.2860 | | 0.0134 |
| ✓ A736287 | Measured | 08/28/2020 17:37:42 | 7511218.8288 | 4693735.8965 | 620.3025 | | 0.0148 |
| ✓ A736288 | Measured | 08/28/2020 17:39:53 | 7511204.3861 | 4693755.2814 | 620.6977 | | 0.0249 |
| ✓ A736289 | Measured | 08/28/2020 17:42:41 | 7511181.1048 | 4693748.1458 | 620.9690 | | 0.0290 |
| ✓ A736290 | Measured | 08/28/2020 17:44:13 | 7511176.9707 | 4693756.3625 | 621.6328 | | 0.0154 |
| ✓ B85497 | Measured | 08/28/2020 18:09:59 | 7511170.8944 | 4693810.8902 | 623.5811 | | 0.0120 |
| ✓ B85498 | Measured | 08/28/2020 18:08:10 | 7511144.1150 | 4693838.8712 | 624.1518 | | 0.0121 |
| ✓ B85499 | Measured | 08/28/2020 18:06:07 | 7511123.8741 | 4693834.8869 | 623.0306 | | 0.0198 |
| ✓ B736272 | Measured | 08/28/2020 18:12:46 | 7511172.0233 | 4693766.1845 | 621.9714 | | 0.0146 |
| ✓ B736275 | Measured | 08/28/2020 18:10:56 | 7511186.7420 | 4693788.9351 | 622.5855 | | 0.0114 |
| ✓ RTCM-Ref 0003 | Reference | 08/28/2020 17:27:04 | 7503168.9298 | 4699391.6087 | 628.0260 | | 0.0000 |



Republika e Kosovës
Republika Kosova-Republic of Kosovo
Qeveria e Kosovës- Vlada Kosova- Government of Kosovo
Ministria e Infrastrukturës dhe Ambientit/ Ministratvo Infrastrukture i Sredine/ Ministry of Infrastructure and Environment
AGJENCIA KADASTRALE E KOSOVËS/KOSOVSKA KATASTARSKA AGENCIJA/ KOSOVO CADASTRAL AGENCY

| | |
|---|---------------------------------------|
| Komuna: Ferizaj | Zona Kadastrale: Lloshkobare |
| Numri i njësis kadastrale: 00908-1,907-4 | Sistemi koordinat: KosovaRef01 |

| Nr | Y | X | H | Kodi | Përshkrimi | Burimi |
|---------|--------------------|--------------------|----------------|-----------|-------------------------|-----------|
| A220086 | 7512362.375 | 4694374.643 | 620.763 | 11 | Monoment | PM |
| 85462 | 7511168.581 | 4693833.135 | 624.590 | 2 | Kunjë - shtyllë metalik | PM |
| 85463 | 7511162.109 | 4693834.970 | 624.548 | 2 | Kunjë - shtyllë metalik | PM |
| 85481 | 7511220.140 | 4693736.581 | 620.286 | 2 | Kunjë - shtyllë metalik | PM |
| 85482 | 7511222.257 | 4693738.038 | 620.273 | 2 | Kunjë - shtyllë metalik | PM |
| 85488 | 7511173.688 | 4693814.791 | 623.747 | 2 | Kunjë - shtyllë metalik | PM |
| 85489 | 7511174.179 | 4693819.724 | 623.840 | 2 | Kunjë - shtyllë metalik | PM |
| 85490 | 7511173.901 | 4693825.322 | 624.205 | 2 | Kunjë - shtyllë metalik | PM |
| 85491 | 7511233.408 | 4693774.915 | 620.754 | 2 | Kunjë - shtyllë metalik | PM |
| 85492 | 7511211.309 | 4693797.147 | 622.572 | 2 | Kunjë - shtyllë metalik | PM |
| 85493 | 7511202.687 | 4693806.158 | 623.332 | 2 | Kunjë - shtyllë metalik | PM |
| 85496 | 7511186.754 | 4693788.926 | 622.589 | 2 | Kunjë - shtyllë metalik | PM |
| 85497 | 7511170.858 | 4693810.895 | 623.587 | 2 | Kunjë - shtyllë metalik | PM |
| 85498 | 7511144.119 | 4693838.872 | 624.151 | 2 | Kunjë - shtyllë metalik | PM |
| 85499 | 7511123.853 | 4693834.863 | 623.070 | 2 | Kunjë - shtyllë metalik | PM |
| 85500 | 7511117.992 | 4693832.963 | 622.748 | 2 | Kunjë - shtyllë metalik | PM |
| 85515 | 7511156.545 | 4693791.194 | 621.971 | 2 | Kunjë - shtyllë metalik | PM |
| 85516 | 7511145.919 | 4693803.158 | 622.183 | 2 | Kunjë - shtyllë metalik | PM |
| 85517 | 7511141.778 | 4693807.571 | 622.366 | 2 | Kunjë - shtyllë metalik | PM |
| 88353 | 7511161.029 | 4693783.957 | 622.439 | 2 | Kunjë - shtyllë metalik | PM |
| 88354 | 7511172.047 | 4693766.179 | 621.989 | 2 | Kunjë - shtyllë metalik | PM |
| 88355 | 7511176.924 | 4693756.395 | 621.633 | 2 | Kunjë - shtyllë metalik | PM |
| 88356 | 7511161.818 | 4693784.656 | 621.668 | 2 | Kunjë - shtyllë metalik | PM |
| 88357 | 7511211.056 | 4693753.051 | 620.737 | 2 | Kunjë - shtyllë metalik | PM |
| 88358 | 7511218.788 | 4693735.998 | 620.302 | 2 | Kunjë - shtyllë metalik | PM |
| 88359 | 7511204.389 | 4693755.272 | 620.698 | 2 | Kunjë - shtyllë metalik | PM |
| 88360 | 7511181.030 | 4693748.158 | 620.969 | 2 | Kunjë - shtyllë metalik | PM |

| Matja e pikave në dy seri | | | | | | | |
|---------------------------|-----------|-------------|-------------|--------|---------|---------|--------|
| Seria | Nr. Pikës | Y | X | H | ΔY | ΔX | ΔP |
| I | 85497 | 7511170.88 | 4693810.91 | 623.59 | -0.0167 | 0.0231 | 0.0285 |
| II | 85497 | 7511170.89 | 4693810.89 | 623.58 | 0.0221 | -0.0010 | 0.0221 |
| I | 85498 | 7511144.137 | 4693838.87 | 624.15 | -0.0408 | -0.0514 | 0.0656 |
| II | 85498 | 7511144.115 | 4693838.871 | 624.15 | 0.0068 | -0.0572 | 0.0576 |
| I | 85499 | 7511123.833 | 4693834.836 | 623.11 | 0.0096 | 0.0274 | 0.0290 |
| II | 85499 | 7511123.874 | 4693834.887 | 623.03 | | | |
| I | 736272 | 7511172.03 | 4693766.127 | 622.01 | | | |
| II | 736272 | 7511172.023 | 4693766.185 | 621.97 | | | |
| I | 736275 | 7511186.752 | 4693788.963 | 622.59 | | | |
| II | 736275 | 7511186.742 | 4693788.935 | 622.59 | | | |

| Koordinatat përfundimtare | | | |
|---------------------------|-------------|-------------|---------|
| Nr | Y | X | H |
| 85497 | 7511170.886 | 4693810.902 | 623.587 |
| 85498 | 7511144.126 | 4693838.871 | 624.151 |
| 85499 | 7511123.854 | 4693834.861 | 623.070 |
| 88354 | 7511172.027 | 4693766.156 | 621.989 |
| 85496 | 7511186.747 | 4693788.949 | 622.589 |

| | | | |
|---|----------------|----------------------|--|
| Gjeodeti / Kompania gjeodete e licencuar: | LIRIDON SEJDIU | Nënshkrimi dhe vula: | |
| Numri i licencës | 140 | | |



Republika e Kosovës
Republika Kosova-Republic of Kosovo
Qeveria e Kosovës- Vlada Kosova- Government of Kosovo

Ministria e Infrastrukturës dhe Ambientit/ Ministrastvo Infrastrukture i Sredine/ Ministry of Infrastructure and Environment

AGJENCIA KADASTRALE E KOSOVËS/KOSOVSKA KATASTARSKA AGENCIJA/ KOSOVO CADASTRAL AGENCY

FORMULARI PËR KORIGJIMIN E SIPËRFAQËS

| | |
|--|------------------------------|
| Gjeodeti / Kompania gjeodete e licencuar: Liridon Sejdiu | Numri i licencës:140 |
| Komuna: Ferizaj | Zona Kadastrale: Lloshkobare |
| Numri i njësisë kadastrale:00908-1 | Numri i lëndës: 194/2020 |

1. Tabela e ndryshimeve të sipërfaqes

| Numri i parcelës | Sipërfaqja faktike (m ²) | Sipërfaqja nga SIKTK-T (m ²) | Ndryshimi (m ²) | Sipërfaqja e korrigjuar (m ²) |
|------------------|---|---|--------------------------------|--|
| 00908-1 | 2716 | 2720 | -4 | 2716 |

Bazuar në procesverbalin e terrenit, pronarët janë pajtuar me pikat definitive kufitare të vendosura në terren nga të cilat edhe është derivuar sipërfaqja definitive që regjistrohet në SIKTK.

Nënshkrimi dhe vula e gjodetit: _____

Data: 29/08/2020



Republika e Kosovës
Republika Kosova-Republic of Kosovo
Qeveria e Kosovës- Vlada Kosova- Government of Kosovo

Ministria e Infrastrukturës dhe Ambientit/ Ministrastvo Infrastrukture i Sredine/ Ministry of Infrastructure and Environment

AGJENCIA KADASTRALE E KOSOVËS/KOSOVSKA KATASTARSKA AGENCIJA/ KOSOVO CADASTRAL AGENCY

RAPORTI TEKNIK

| | |
|---|--|
| Gjeodeti / Kompania gjeodete e licencuar: Liridon Sejdiu | Numri i licencës: 140 |
| Komuna: Ferizaj | Zona Kadastrale: Lloshkobare |
| Numri i njësisë kadastrale: 00907-4,00908-1 | Lloji i lëndës: Bashkim i parcelave |
| | |

Bazuar në kërkesën e palës **z. BUJAR (BAJRUSH) MISINI** me numër biznesi **1170142531** të parashtruar me datën **25/08/2020**, është bërë kërkesa për marrjen e produkteve kadastrale në Zyrën Kadastrale Komunale **Ferizaj** me datë **26/08/2020**.

Pas analizimit të të dhënave me datë **28/08/2020** janë realizuar matjet në terren, për (**ndarjen/bashkimin**) e parcelave bazuar në (**gjendjen faktike/sipërfaqe të barazuara**).

Matjet në terren janë realizuar me instrument (GPS Leica 1230), ku fillimisht është bërë matja e pikës kontrolluese **22086** pastaj matjet janë realizuar bazuar në kornizën AKK nr.: 2020/01

Matje të dyfishta kontrolluese janë realizuar në pikat numër **85497,85498,85499,88354,85496**

Sfidat gjatë realizimit të

matjeve: _____

Matje të dyfishta kontrolluese janë realizuar në pikat numër **85497,85498,85499,88354,85496**.

Raporti në formë tabelare:

| Parcela para ndarjes/bashkimit | Sipërfaqja (m ²) | Korigjimi i sipërfaqe (po/jo) | Parcela pas ndarjes/bashkimit | Sipërfaqja (m ²) |
|--------------------------------|------------------------------|-------------------------------|-------------------------------|------------------------------|
| 00907-4 | 1458 | JO | 1003-0 | 4174 |
| 00908-1 | 2716 | PO | | |

Nënshkrimi dhe vula e gjodetit: _____

Data: **29/08/2020**



Republika e Kosovës
Republika Kosova-Republic of Kosovo
Qeveria - Vlada - Government

MINISTRIA E EKONOMISË DHE AMBIENTIT / MINISTARSTVO EKONOMIJE I ŽIVOTNE SREDINE / MINISTRY OF ECONOMY AND ENVIRONMENT
AGJENCIA KADASTRALE E KOSOVËS / KATASTARSKA AGENCIJA KOSOVA / KOSOVO CADASTRAL AGENCY

CERTIFIKATË / CERTIFIKAT / CERTIFICATE

PERSONI / OSOBA / PERSON : MISINI BAJRUSH

| | |
|--|------------------------------|
| Numri i lëndës / Broj Predmet / Case Referent Number: | 68292-2020 |
| Data dhe koha e lëshimit / Datum i vreme izdavanja / Date and time of submission: | 25.08.2020 - 13:15 |
| Komuna / Opština / Municipality: | Ferizaj / Uroševac / Ferizaj |
| Zyra Kadastrale Komunale / Opštinska Katastarska Kancelarija / Municipal Cadastral Office: | Ferizaj / Uroševac / Ferizaj |

A. TË DHËNAT PËR PERSONIN / PODACI O OSOBI / PERSON'S DATA

| Mbiemri/Emri i afarizmit (biznesit) Prezime/ Naziv poslovanja (biznisa) Last Name / Business Name | Emri Ime First Name | Emri i babait Ime oca Father's Name | Gjinia Pol Gender | Nr. personal/ biznesit Lični broj/broj poslovanja ID. No. | Shteti i shtetësisë apo regjistrimit Država državljanstva ili uknjiženja Country of citizenship | Ditëlindja/Data e themelimit Rodendan/Dan osnivanja Date of Birth/Establishmen t | Krijuar më datën Uradjeno na dan Created On | Azhuruar Ažurirano Updated |
|---|---------------------------|---|-------------------------------|--|--|--|---|----------------------------------|
| MISINI | BAJRUSH | UKË | Mashkull / Musko / Male | 101306766 | KOSOVA / KOSOVA / KOSOVO | 08.03.1934 | | 10.08.2015 |

A.1 ADRESA E PERSONIT / ADRESA OSOBE / PERSON'S ADDRESS

| Vendbanimi Prebivaliste Resident | Kodi Postal Poštanski Kod Postal Code | Hollësitë e adresës Pojedinosti adrese Address Details | Adresa tjetër Druga adresa Other address | Azhuruar Ažurirano Updated |
|--|---|--|--|----------------------------------|
| LLOSHKOBARE / LAŠKOBARE / BALÇAK | | | FERIZAJ | 10.08.2015 |

B. NJESIA KADASTRALE/ KATASTARSKA JEDINICA/CADASTRAL UNIT

| Njësie kadastrale Katastarska jedinica Cadastral unit | Komuna / Opština / Municipality | Zona kadastrale Katastarska zona Cadastral zone | Lloji i njësisë Vrsta jedinice Unit type | Tip i pronës Tip imovine Property Type / Lloji i pronës Vrsta imovine Property kind | Kati/ Katet Br.Sprat a/ Spratova Floor number | Vendi i quajtur Zvano mesto Place name | Sipërfaqja Površina Area | Shfrytezimi aktual/Kultura- klasa Aktuelna upotreba/ Kultura-klasa Actual use/Culture-class | Pjesa e pronës Deo imovine Share quota | Lloji i së drejtës Vrsta prava Type of the right | Azhuruar Ažurirano Updated |
|---|---------------------------------------|---|--|---|---|--|--------------------------------|--|--|---|----------------------------------|
| P-72217056-00906-7 | Ferizaj / Uroševac / Ferizaj | LLOSHKOBAR E / LAŠKOBARE / BALÇAK | PARCELË / PARCELA / parcel | Pronë private Privatna Imovina Privately owned Land / R | | TOPOLA / TOPOLA / TOPOLA | 137 | Bujqësore - Livadhet - Livadh I Klasës 2 // Poljoprivredno - Livade - Livada 2 Klase // Agriculture - meadow - 2nd Class Meadow // | 2 / 6 | Bashkë Posedim / SuDrzavina / co-possessor | |
| P-72217056-00907-1 | Ferizaj / Uroševac / Ferizaj | LLOSHKOBAR E / LAŠKOBARE / BALÇAK | PARCELË / PARCELA / parcel | Pronë private Privatna Imovina Privately owned Land / R | | TOPOLA DO SEJDE / TOPOLA DO SEJDE / TOPOLA DO SEJDE | 348 | Infrastruktura - Rrugë - // Infrastruktura - Put - // Infrastructure - Road - // | 2 / 6 | Bashkë Posedim / SuDrzavina / co-possessor | 07.03.2019 |
| P-72217056-00907-4 | Ferizaj / Uroševac / Ferizaj | LLOSHKOBAR E / LAŠKOBARE / BALÇAK | PARCELË / PARCELA / parcel | Pronë private Privatna Imovina Privately owned Land / R | | TOPOLA DO SEJDE / TOPOLA DO SEJDE / TOPOLA DO SEJDE | 1458 | Bujqësore - Livadhet - Livadh I Klasës 2 // Poljoprivredno - Livade - Livada 2 Klase // Agriculture - meadow - 2nd Class Meadow // | 1 / 1 | Posedim individual / Individualna Drzavina / single possessor | 11.04.2019 |
| P-72217056-00908-1 | Ferizaj / Uroševac / Ferizaj | LLOSHKOBAR E / LAŠKOBARE / BALÇAK | PARCELË / PARCELA / parcel | Pronë private Privatna Imovina Privately owned Land / R | | TOPOLA / TOPOLA / TOPOLA | 2720 | Bujqësore - Arat - Arë E Klasës 4 // Poljoprivredno - Njive - Njiva 4 Klase // Agriculture - Arable - 4th Class Arable Land // | 1 / 1 | Posedim individual / Individualna Drzavina / single possessor | 23.03.2018 |
| P-72217056-00908-3 | Ferizaj / Uroševac / Ferizaj | LLOSHKOBAR E / LAŠKOBARE / BALÇAK | PARCELË / PARCELA / parcel | Pronë private Privatna Imovina Privately owned Land / R | | TOPOLA / TOPOLA / TOPOLA | 639 | Bujqësore - Arat - Arë E Klasës 4 // Poljoprivredno - Njive - Njiva 4 Klase // Agriculture - Arable - 4th Class Arable Land // | 1 / 1 | Posedim individual / Individualna Drzavina / single possessor | 23.03.2018 |

| | | | | | | | | | | | |
|--------------------|------------------------------------|--|---|--|--|--------------------------------|------------|---|--------------|---|------------|
| P-72217056-00908-4 | Ferizaj / Uroševac / Ferizaj | LLOSHKOBAR E / LAŠKOBARE / BALÇAK | PARCELË / PARCELA / parcel | Pronë private Privatna Imovina Privately owned Land /R | | TOPOLA / TOPOLA / TOPOLA | 588 | Bujqësore - Arat - Arë E Klasës 4 // Poljoprivredno - Njive - Njiva 4 Klasc // Agriculture - Arable - 4th Class Arable Land // | 1 / 1 | Posedim individual / Individualna Drzavina / single possessor | 23.03.2018 |
|--------------------|------------------------------------|--|---|--|--|--------------------------------|------------|---|--------------|---|------------|