Republika e Kosovës
Republika Kosova-Republic of Kosova
Qeveria -Vlada-Government
Ministria e Mjedisit dhe Planifikimit Hapësinor /Ministarstvo Sredine i Prostornog Planiranja/Ministry of Environment and Spatial Planning
AGJENCIA KADASTRALE E KOSOVËS/ KATASTARSKA AGECIJA KOSOVA/ KOSOVA CADASTRAL AGENCY

Zyra kadastrale komunale / Opštinska katastarska kancelarija: Ferizaj

Nr. i njësisë kadastrale / Br. katastarske jedinice : 907-4,908-1

Zona kadastrale / Katastarska zona: Lloshkobare

Numri i lëndës / Broj predmeta: _____

Lloji i njësisë kadastrale / Vrsta katastarske jedinice : Parcel

Shkalla e zvoglimit / Razmera plana : 1:1000

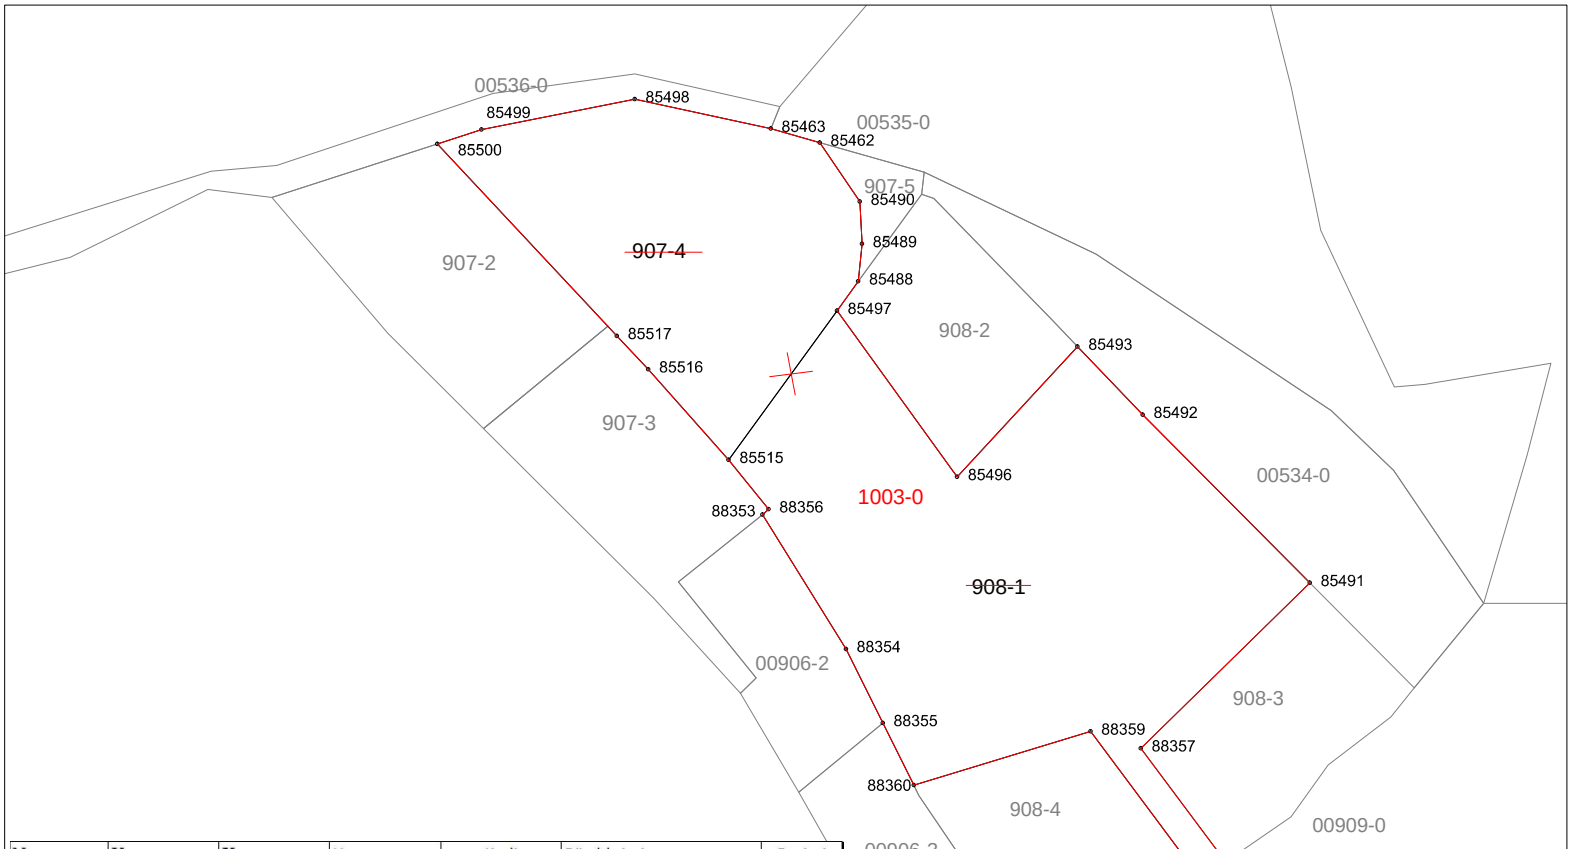

Nr	Y	X	H	Kodi	Përshkrimi	Burimi
A220086	**7512362.375**	**4694374.643**	**620.763**	**11**	**Monoment**	**PM**
85462	7511168.581	4693833.135	624.590	2	Kunjë - shtyllë metalik	PM
85463	7511162.109	4693834.970	624.548	2	Kunjë - shtyllë metalik	PM
85481	7511220.140	4693736.581	620.286	2	Kunjë - shtyllë metalik	PM
85482	7511222.257	4693738.038	620.273	2	Kunjë - shtyllë metalik	PM
85488	7511173.688	4693814.791	623.747	2	Kunjë - shtyllë metalik	PM
85489	7511174.179	4693819.724	623.840	2	Kunjë - shtyllë metalik	PM
85490	7511173.901	4693825.322	624.205	2	Kunjë - shtyllë metalik	PM
85491	7511233.408	4693774.915	620.754	2	Kunjë - shtyllë metalik	PM
85492	7511211.309	4693797.147	622.572	2	Kunjë - shtyllë metalik	PM
85493	7511202.687	4693806.158	623.332	2	Kunjë - shtyllë metalik	PM
85496	7511186.754	4693788.926	622.589	2	Kunjë - shtyllë metalik	PM
85497	7511170.858	4693810.895	623.587	2	Kunjë - shtyllë metalik	PM
85498	7511144.119	4693838.872	624.151	2	Kunjë - shtyllë metalik	PM
85499	7511123.853	4693834.863	623.070	2	Kunjë - shtyllë metalik	PM
85500	7511117.992	4693832.963	622.748	2	Kunjë - shtyllë metalik	PM
85515	7511156.545	4693791.194	621.971	2	Kunjë - shtyllë metalik	PM
85516	7511145.919	4693803.158	622.183	2	Kunjë - shtyllë metalik	PM
85517	7511141.778	4693807.571	622.366	2	Kunjë - shtyllë metalik	PM
88353	7511161.029	4693783.957	622.439	2	Kunjë - shtyllë metalik	PM
88354	7511172.047	4693766.179	621.989	2	Kunjë - shtyllë metalik	PM
88355	7511176.924	4693756.395	621.633	2	Kunjë - shtyllë metalik	PM
88356	7511161.818	4693784.656	621.668	2	Kunjë - shtyllë metalik	PM
88357	7511211.056	4693753.051	620.737	2	Kunjë - shtyllë metalik	PM
88358	7511218.788	4693735.998	620.302	2	Kunjë - shtyllë metalik	PM
88359	7511204.389	4693755.272	620.698	2	Kunjë - shtyllë metalik	PM
88360	7511181.030	4693748.158	620.969	2	Kunjë - shtyllë metalik	PM

Rilevoi / Snimio: LIRIDON SEJDIU
(emri dhe mbiemri i gjeodetit/kompanisë/ ime i prezime geodeta/ kompanije)

Aprovoi / Usvojio: _____
(emri dhe mbiemri i përsonit zyrtar/ ime i prezime sluzbenog lica)

Nr. i licencës / Br. licence: 140

V.V.

Nënshkrimi / Potpis: _____

Nënshkrimi / Potpis: _____

Data e rilevimit / Datum snimanja: 28.08.2020

Data e aprovimit / Datum usvajanja: _____